



*Общество с ограниченной ответственностью
"Хрустальный"*

Свидетельство №СРО-П-201-04.06.2018-3827046991-277 от 28.03.2019 г

ЗАКАЗЧИК: ООО СЗ "Хрустальный Парк"

*Микрорайон «Хрустальный Парк» и объекты инженерной инфраструктуры, расположенный на
11 км Байкальского тракта.
13-я очередь строительства (квартал "Датский")*



Тип 2в. Многоквартирный жилой дом 13-11

ЭСКИЗНЫЙ ПРОЕКТ

ХП.13 – 2в – АР


Иркутск 2023

План этажа на отм. 0,000

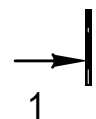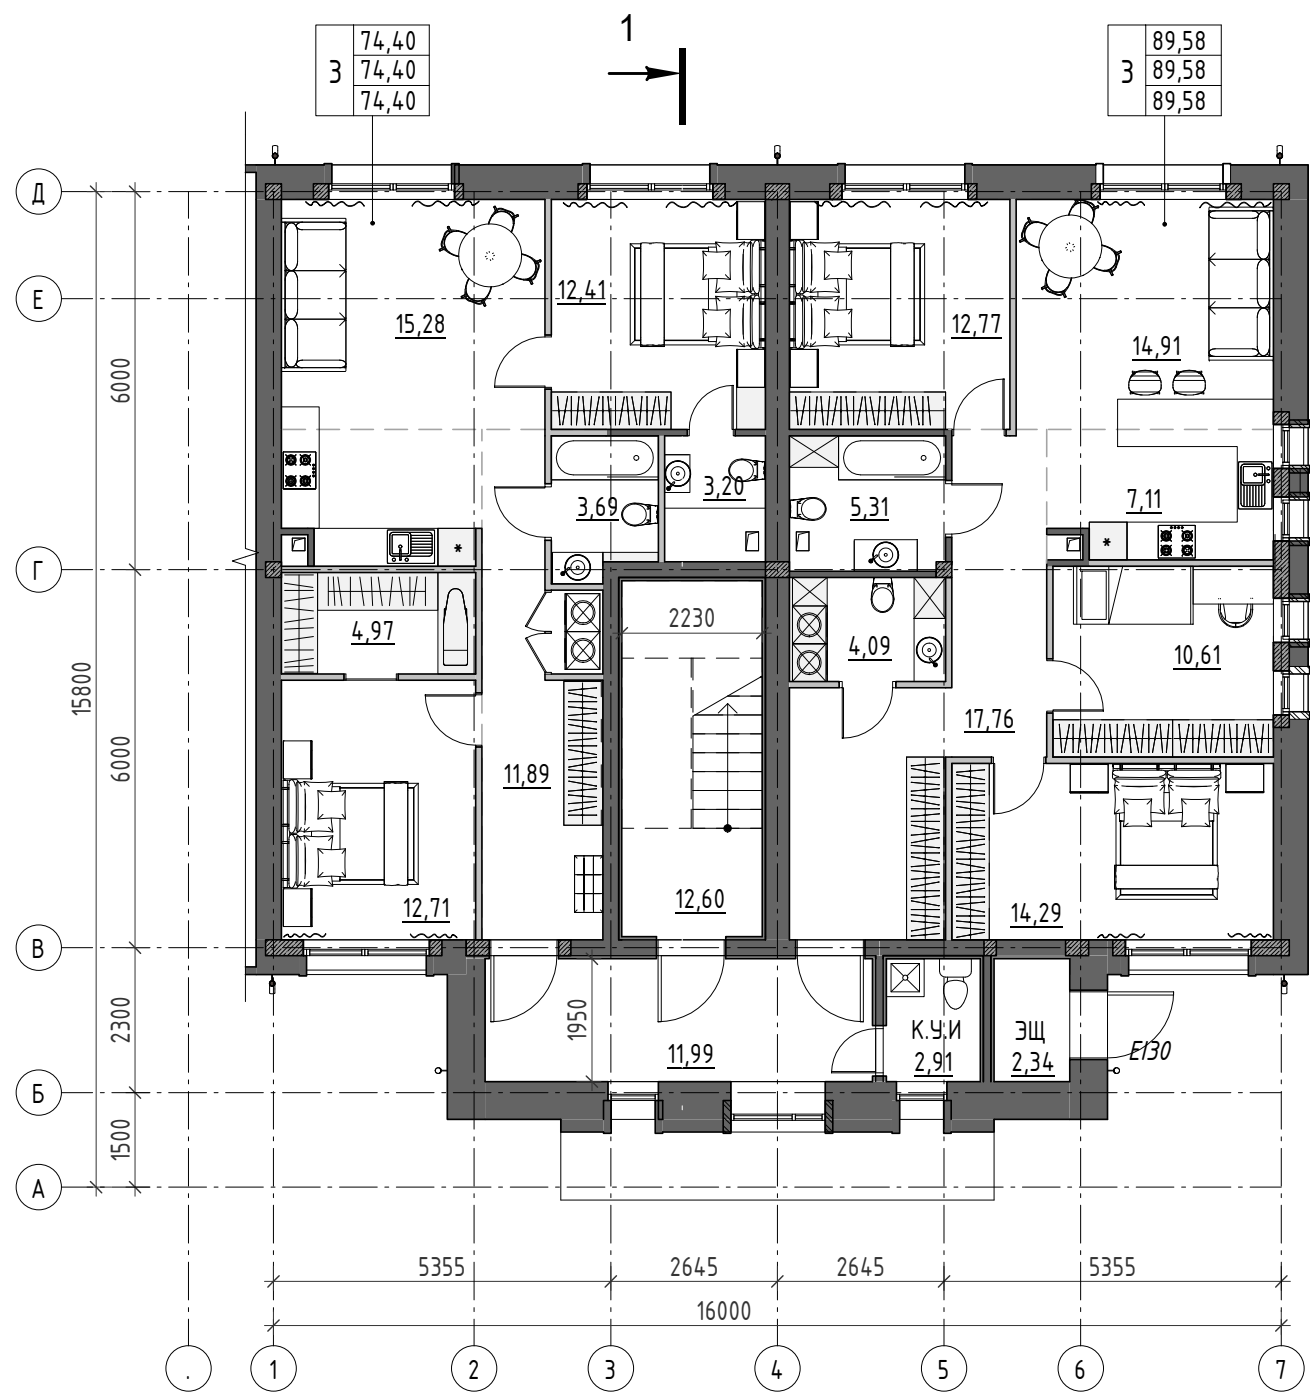


Примечания:
1. Площади должны быть уточнены при разработке стадии П
2. При разработке стадии П уточнить расположение помещений, сетей

План этажа на отм. +3,000


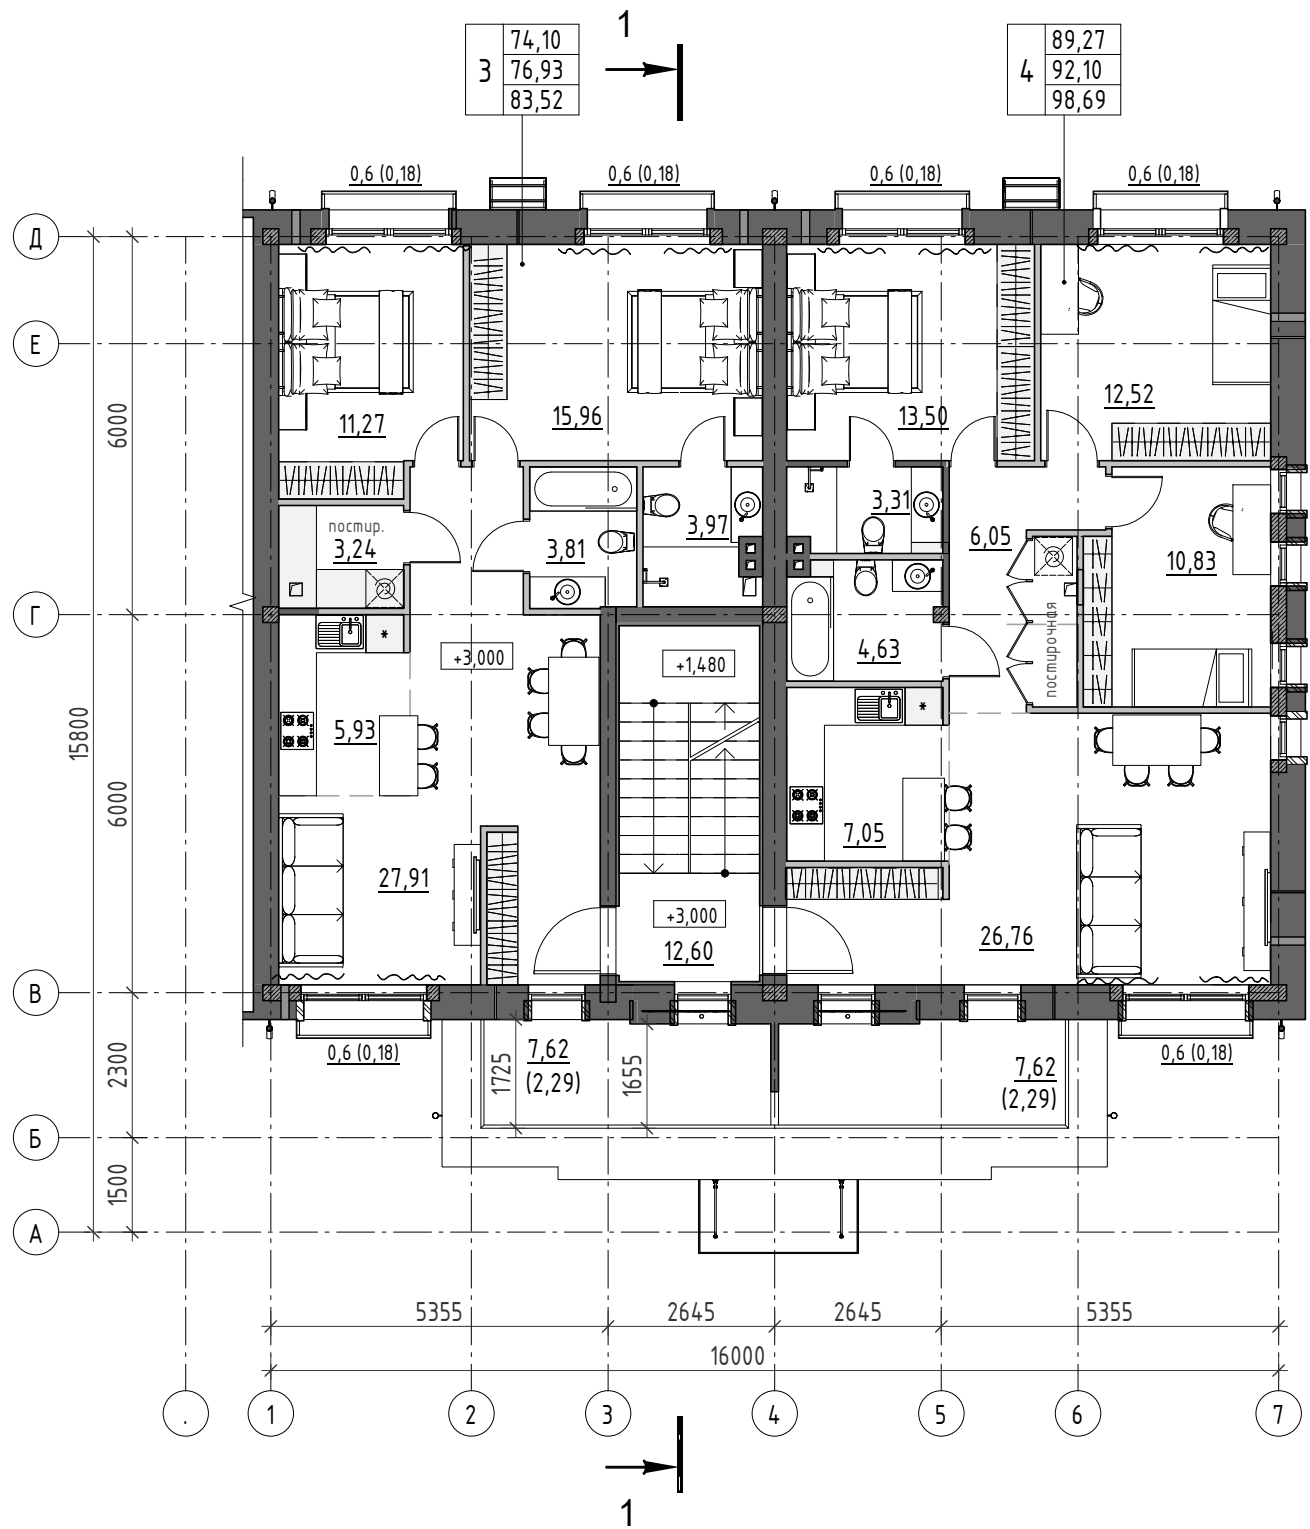


						ХП.13 – 26 – АР			
						Микрорайон «Хрустальный Парк» и объекты инженерной инфраструктуры, расположенный на 11 км Байкальского тракта. 13-я очередь строительства (квартал "Датский")			
Изм.	Кол.уч	Лист	№ док.	Подпись	Дата				
Разработал	Панкова				03.23	Тип 26. Многоквартирный жилой дом 13-11	Стадия	Лист	Листов
					03.23			101	
					03.23				
					03.23				
						План на отм. 0,000, +3,000 (вариант планировочного решения)	 №СРО- П-201-04062018-3827046991-277		

План на отм. +6,000

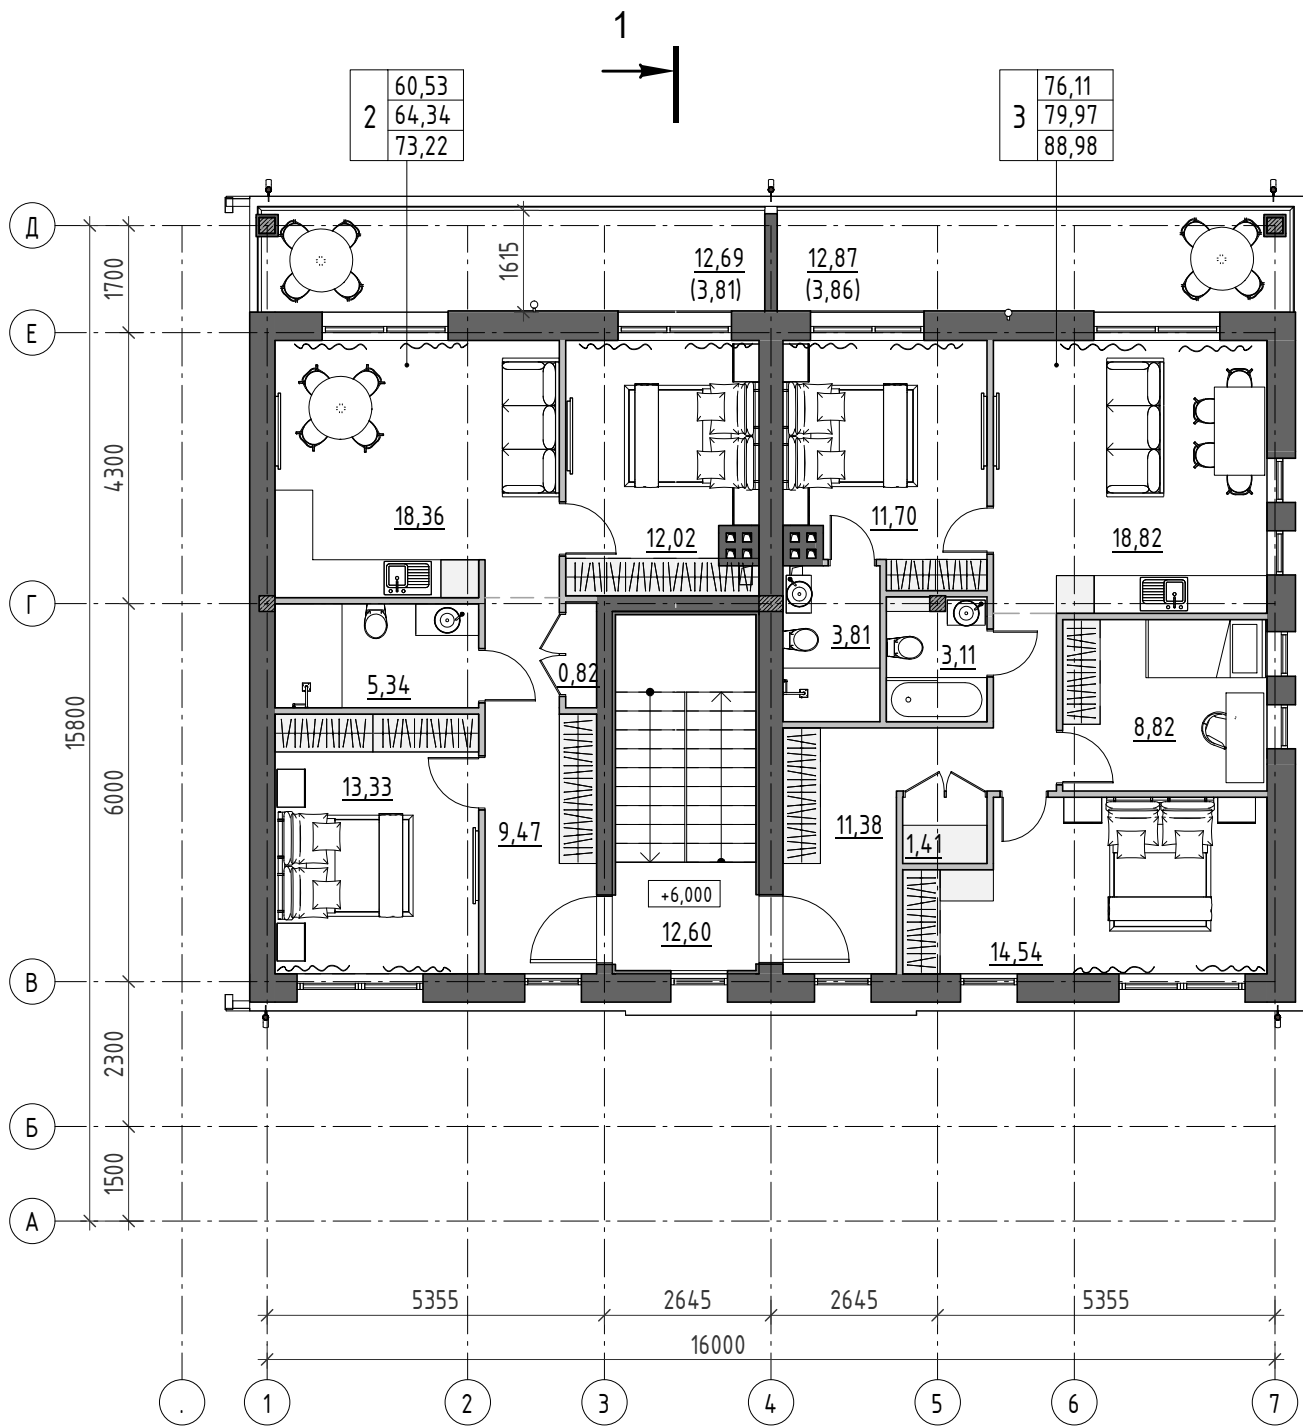

План кровли

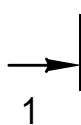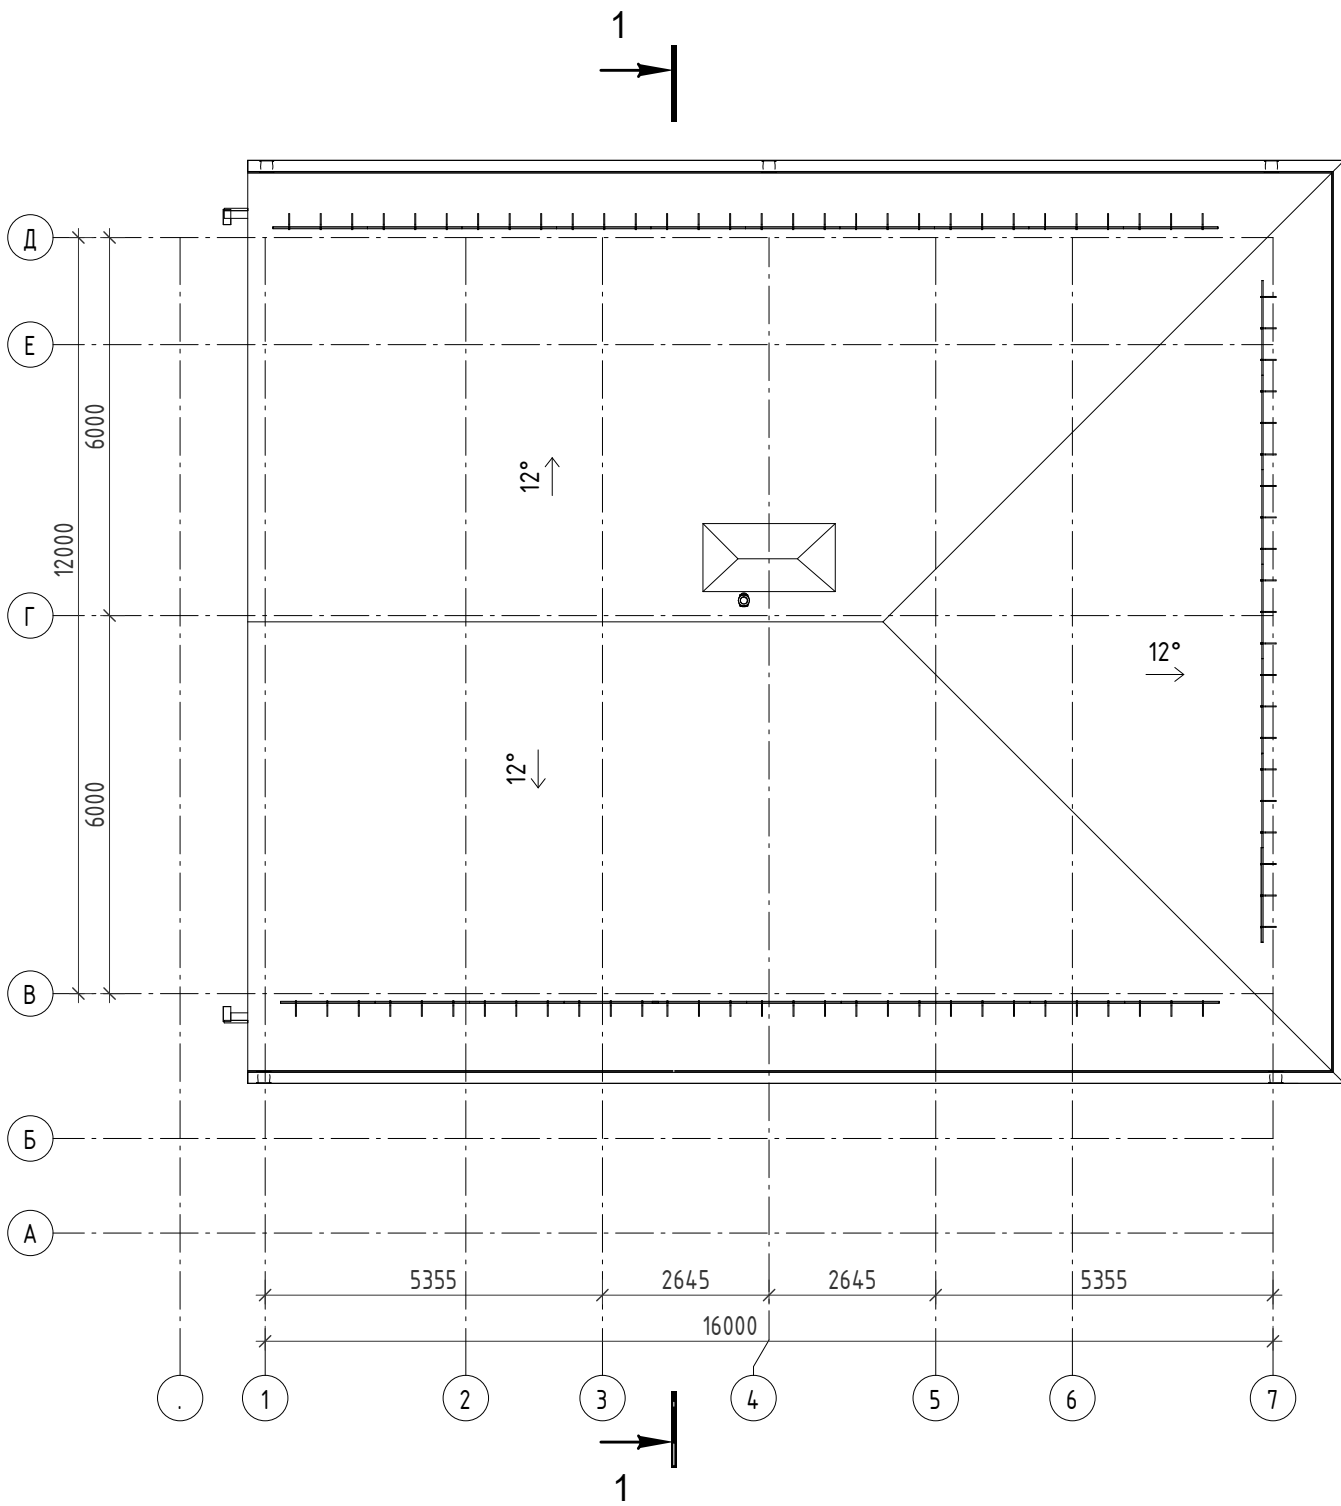


Примечания:
1. Площади должны быть уточнены при разработке стадии П
2. При разработке стадии П уточнить расположение помещений, сетей

						ХП.13 – 26 – АР			
						Микрорайон «Хрустальный Парк» и объекты инженерной инфраструктуры, расположенный на 11 км Байкальского тракта. 13-я очередь строительства (квартал “Датский”)			
Изм.	Кол.уч	Лист	№ док.	Подпись	Дата	Тип 26. Многоквартирный жилой дом 13-11	Стадия	Лист	Листов
Разработал	Панкова				03.23			102	
					03.23				
					03.23				
					03.23				
						План на отм. +6,000 (вариант планировочного решения), план кровли	 ОБЩЕСТВО С ОГРАНИЧЕННОЙ ОТВЕТСТВЕННОСТЬЮ ХРУСТАЛЬНЫЙ www.trustalini.ru № СРО- П-201-04062018- 3827046991-277		

Инв. № подл.	Взам. инв. №
Подпись и дата	

Разрез 1-1

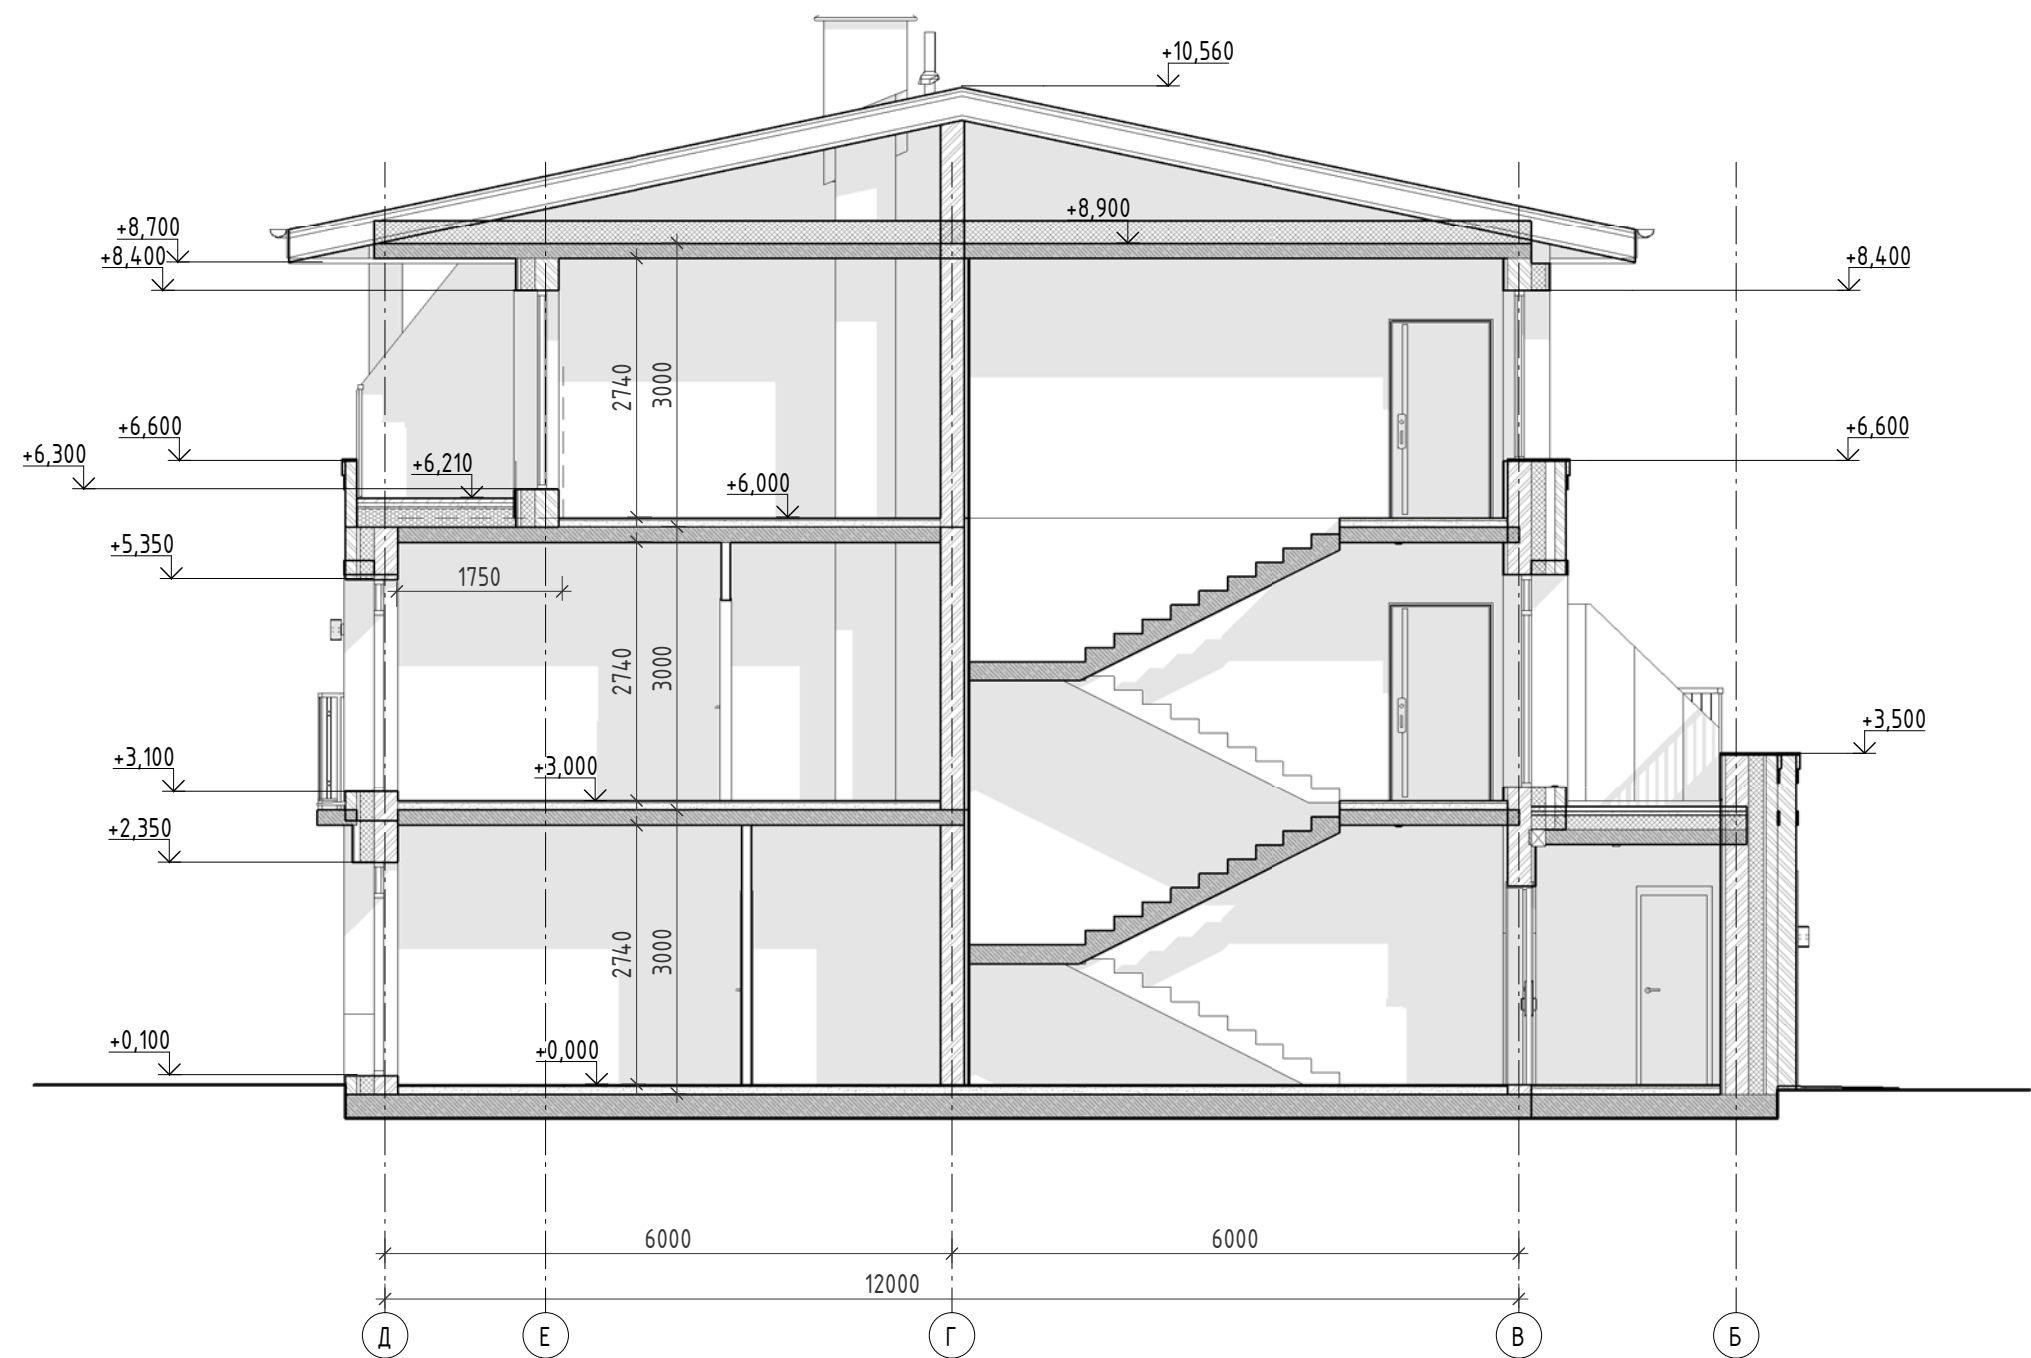

Примечание:
1. Разрез указан для справки, уточнить расположение конструктивных элементов, составов стен, полов и кровель в стадии П

						ХП.13 – 2б – АР			
						Микрорайон «Хрустальный Парк» и объекты инженерной инфраструктуры, расположенный на 11 км Байкальского тракта. 13-я очередь строительства (квартал “Датский”)			
Изм.	Кол.уч	Лист	№ док.	Подпись	Дата	Тип 2б. Многоквартирный жилой дом 13-11	Стадия	Лист	Листов
Разработал	Панкова				03.23			103	
					03.23				
					03.23				
					03.23				
						Разрез 1-1	 ДЕЗАКРЕДИТАЦИЯ ГРУППЫ № СРО- П-201-04062018- 3827046991-277		

Фасад 1-7



Фасад 7-1




Ведомость отделки фасада

Поз. отделки	Наименование элемента фасада	Наименование материала отделки	Наименование и номер эталона цвета или образец колера	Примечание
1	Наружные стены	Кирпич облицовочный 1НФ	Белый	
2	Наружные стены	Кирпич облицовочный 1НФ	Красная гвардия Флэш Нео	
3	Наружные стены	Алюмокомпозитные панели	Графитовый серый. RAL 7024	
4	Наружные стены	Алюмокомпозитные панели	Текстура дерева	
5	Кровля	Металлочерепица	Графитовый серый. RAL 7024	
6	Водосточная система	ПВХ	RR 32 Matt	
8	Профиль окон	ПВХ	Антрацитово-серый. RAL 7016 / Белый. RAL 9003	

- Примечания:
- Фасадные материалы уточнить в стадии П
 - Подшивка софитов стальные перфорированные софиты цвет графит RAL7024.

						ХП.13 – 26 – АР			
						Микрорайон «Хрустальный Парк» и объекты инженерной инфраструктуры, расположенный на 11 км Байкальского тракта. 13-я очередь строительства (квартал “Датский”)			
Изм.	Кол.уч	Лист	№ док.	Подпись	Дата				
Разработал	Панкова				03.23	Тип 26. Многоквартирный жилой дом 13–11	Стадия	Лист	Листов
					03.23			104	
					03.23				
					03.23				
						Фасад 1–7, 7–1. Ведомость отделки фасада	 ДЕПАРТАМЕНТ ГОРОДСКОГО УПРАВЛЕНИЯ ХРУСТАЛЬНЫЙ www.hrustalnyi.ru №СРО– П–201–04062018– 3827046991–277		

Фасад А-Д

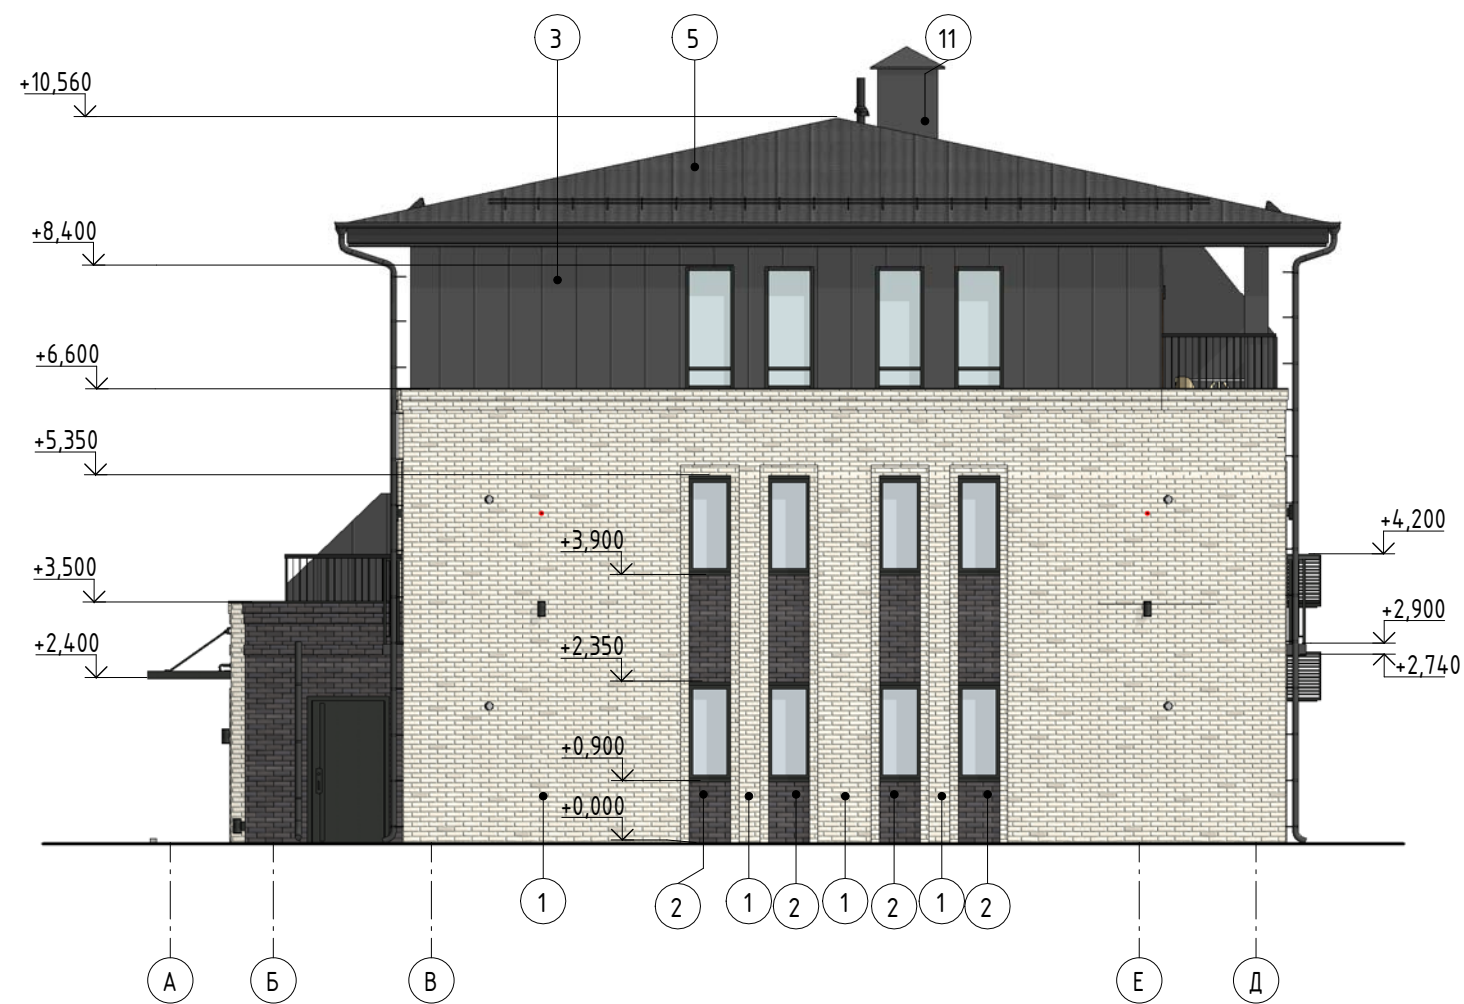

Инв. № подл.	Подпись и дата	Взам. инв. №

						ХП.13 – 28 – АР			
						Микрорайон «Хрустальный Парк» и объекты инженерной инфраструктуры, расположенный на 11 км Байкальского тракта. 13-я очередь строительства (квартал "Датский")			
Изм.	Кол.уч.	Лист	№ док.	Подпись	Дата	Тип 28. Многоквартирный жилой дом 13-11	Стадия	Лист	Листов
Разработал		Панкова			03.23		Р	105	
					03.23				
					03.23				
					03.23				
						Фасад А-Д	 №СРО-П-201-04062018-3827046991-277		











