



План 1 этажа на отм. 0,000

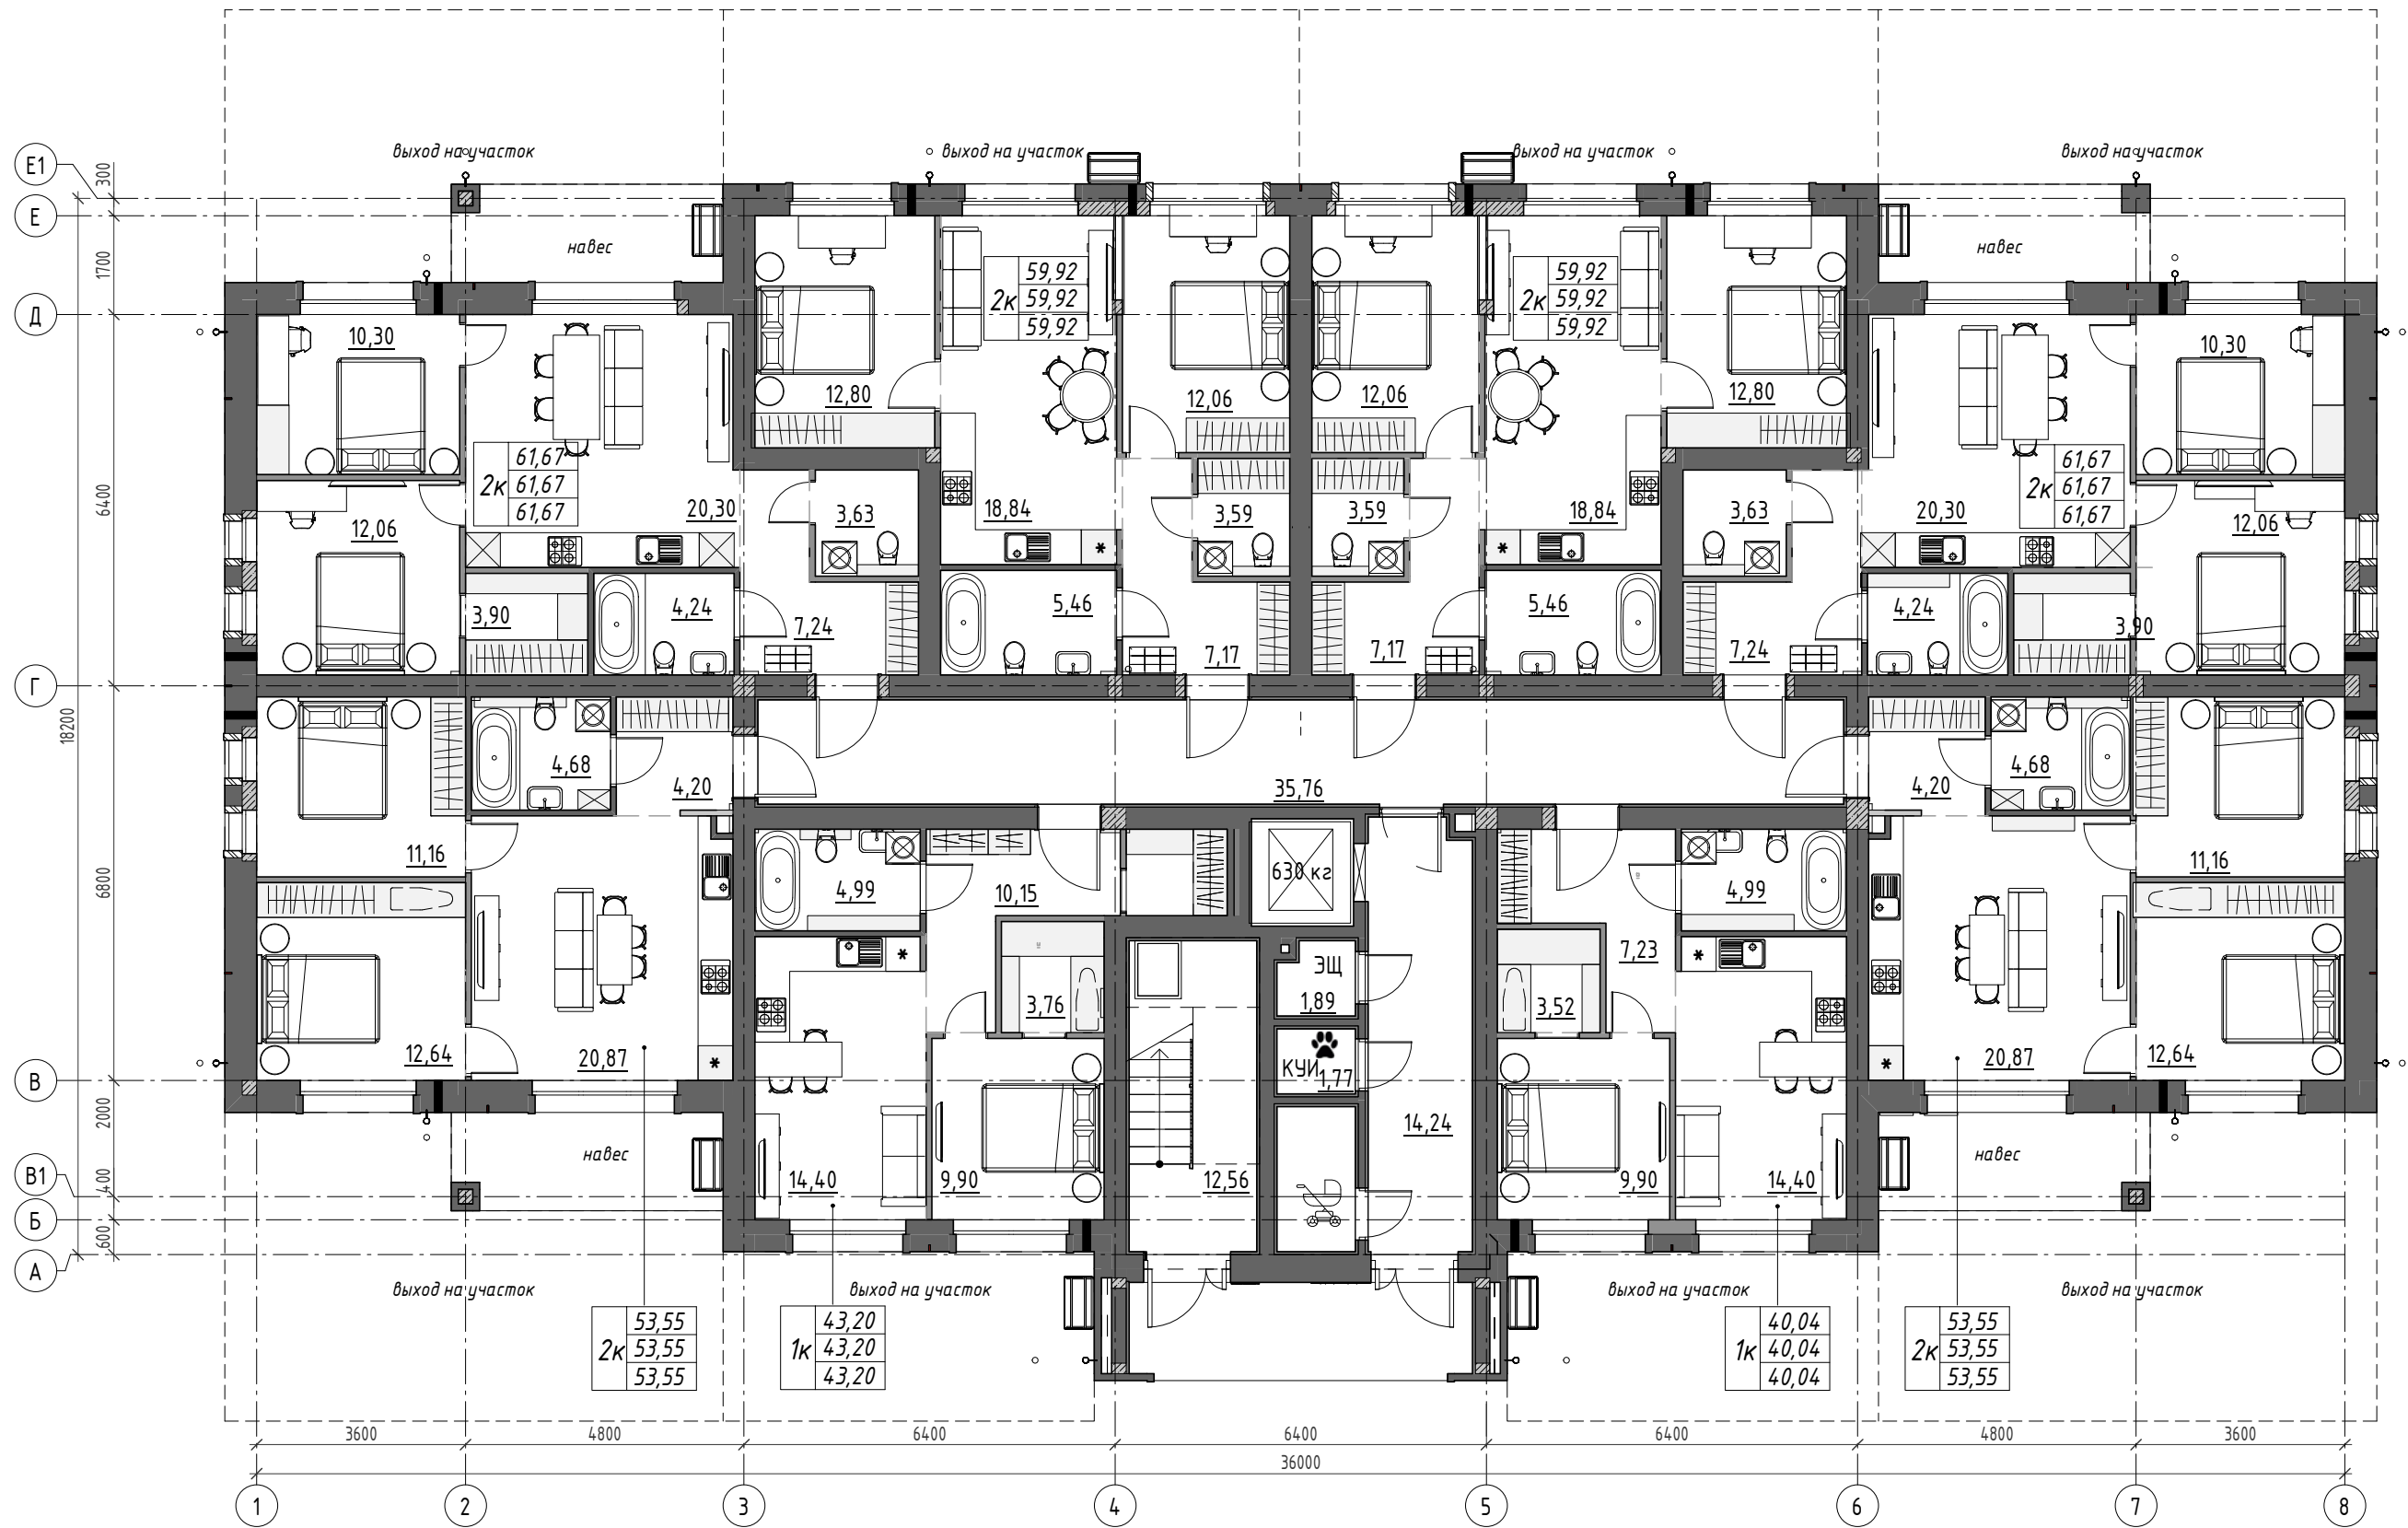

- зона хранения велосипедов (подвесное хранение)
- зона хранения колясок
- мойка лап животных

						ХП.15-1 – АР			
						Микрорайон «Хрустальный Парк» и объекты инженерной инфраструктуры, расположенные на 11 км Байкальского тракта. 15-я очередь строительства (квартал “Датский”)			
Изм.	Кол.уч	Лист	№ док.	Подпись	Дата	Тип 1 Многоквартирные жилые дома 15-1, 15-2	Стадия	Лист	Листов
Разработал	Панкова				02.23		100.2		
Разработал	Панкова				02.23				
					02.23				
					02.23				
						План 1 этажа на отм. 0,000 (вариант планировочного решения)	 дополнительные сведения и контакты ХРУСТАЛЬНЫЙ ПАРК www.hrustalnyi.ru	№ СРО-П-201-04062018 -3827046991-277	


План 2 этажа на отм. +3,000

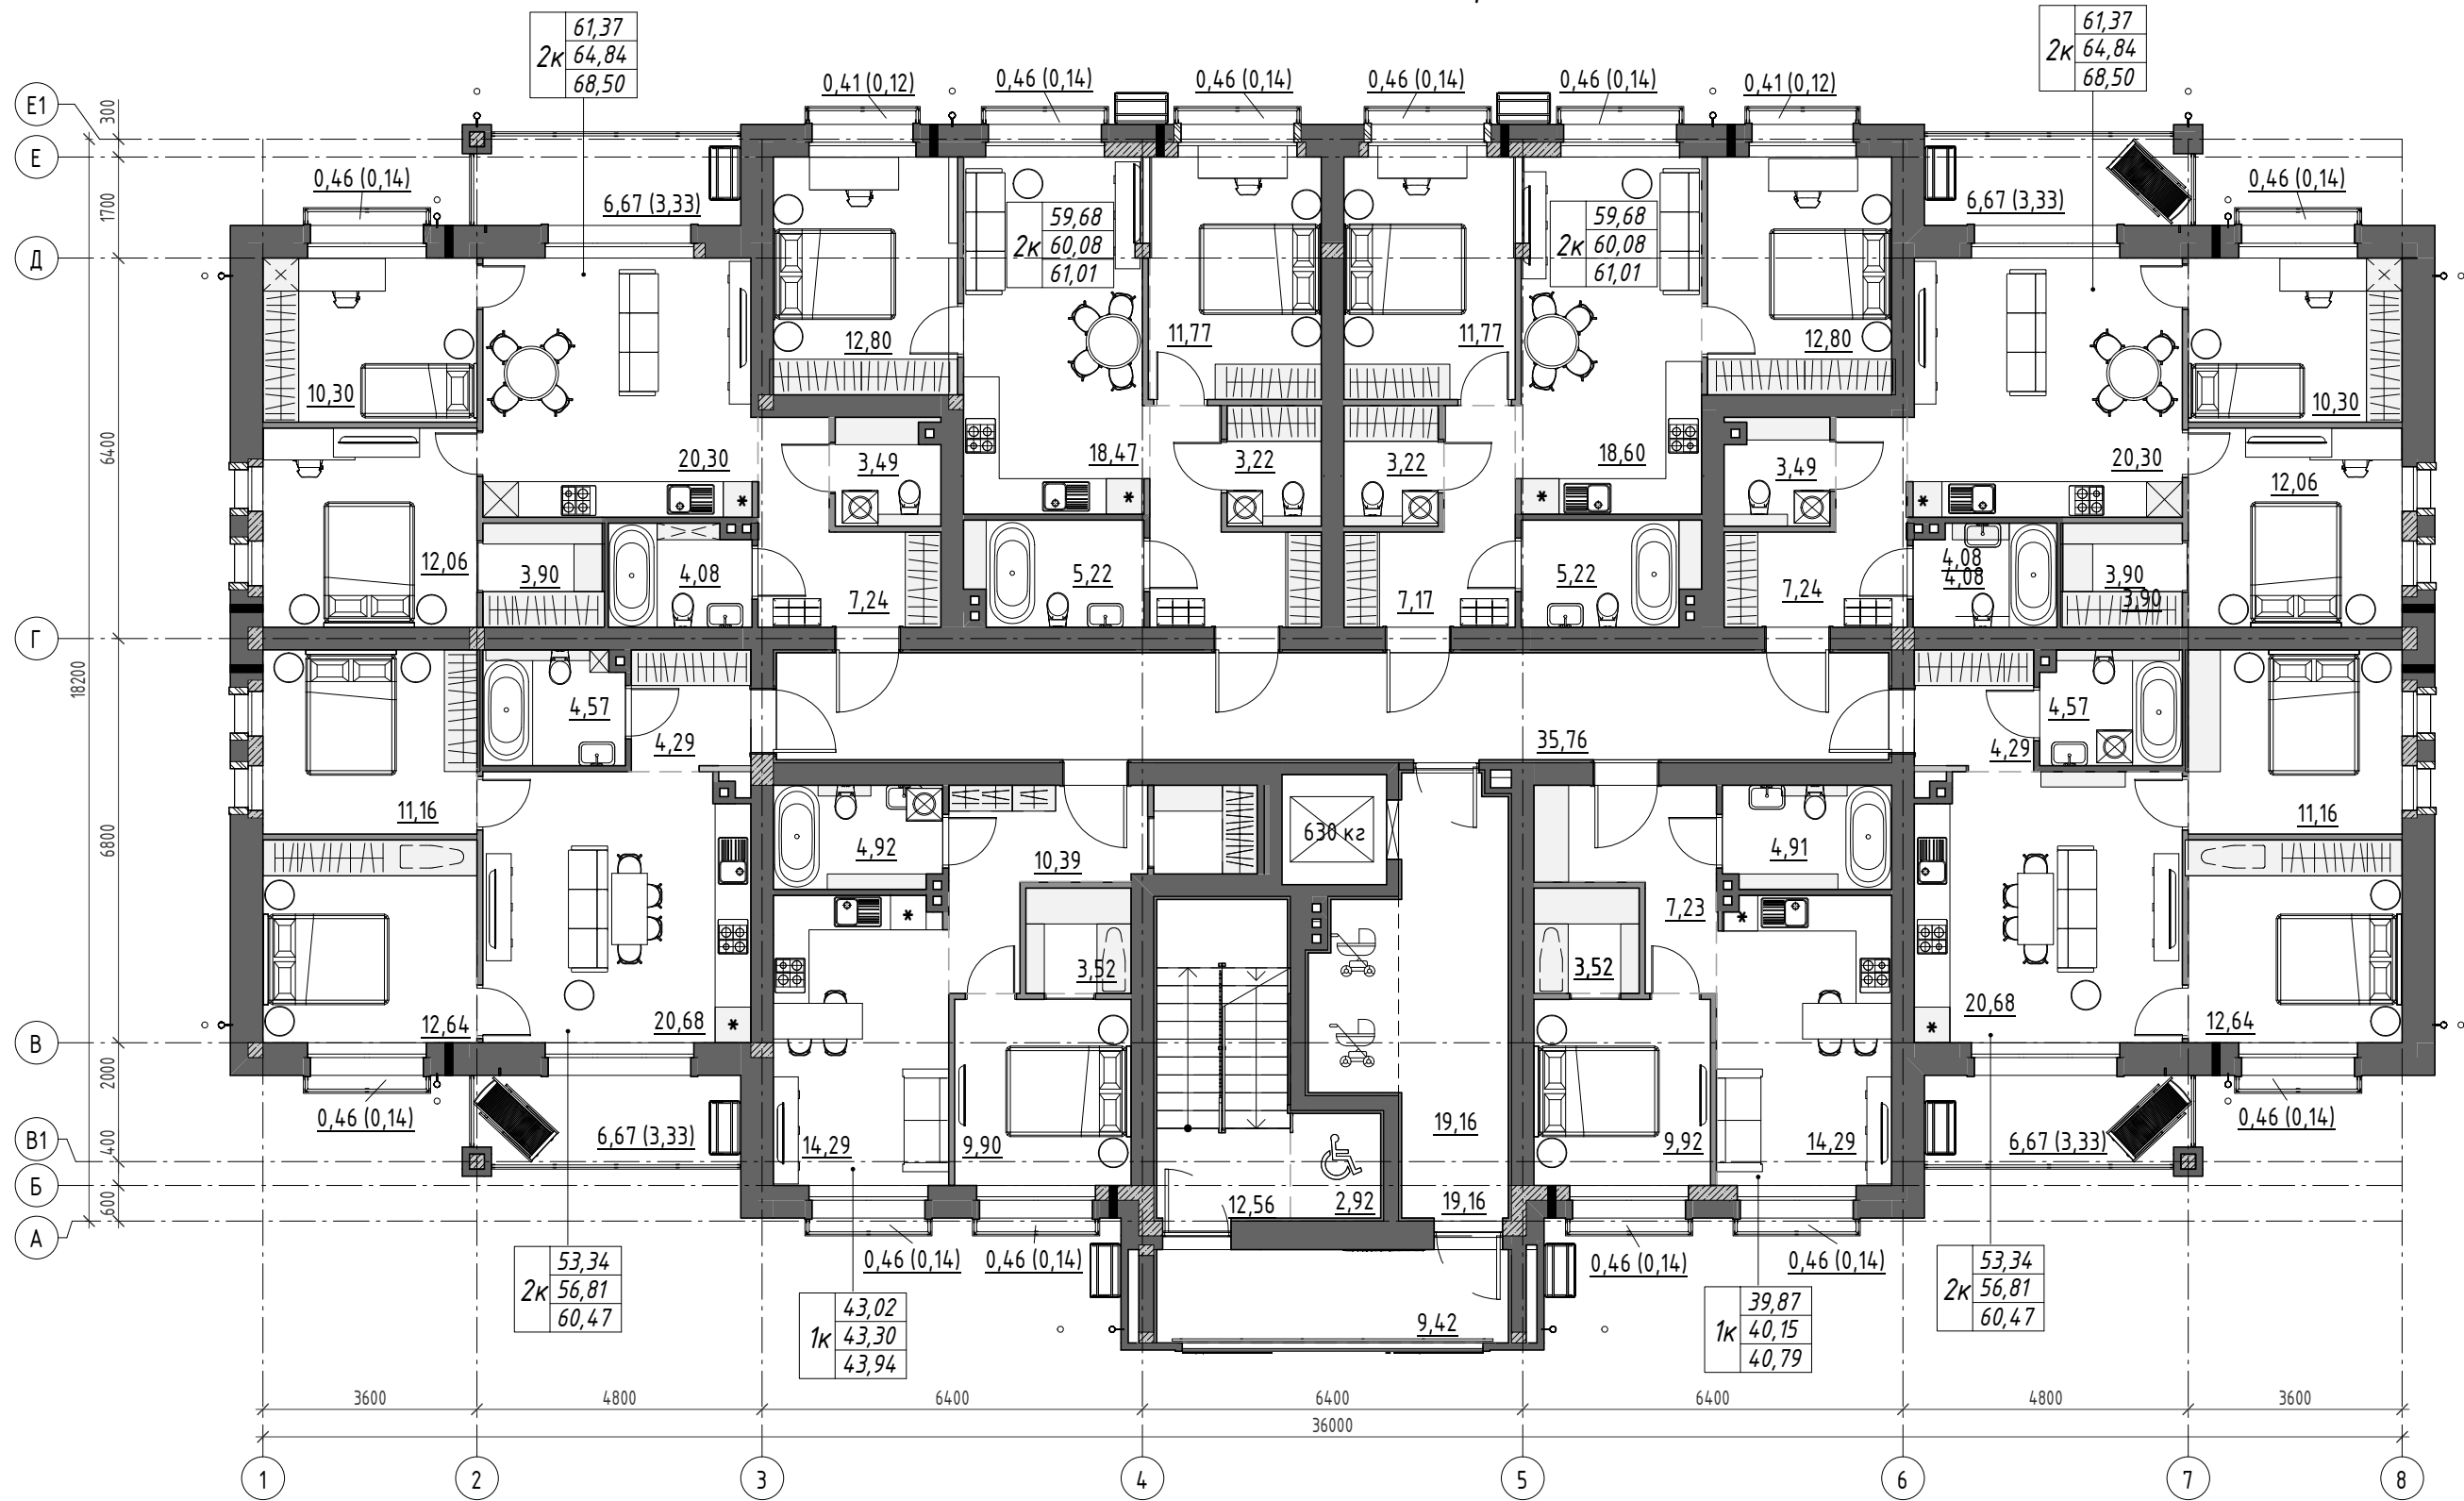

Взам. инв. №	
Подпись и дата	
Инв. № подл.	

						ХП.15-1 – АР			
						Микрорайон «Хрустальный Парк» и объекты инженерной инфраструктуры, расположенные на 11 км Байкальского тракта. 15-я очередь строительства (квартал "Датский")			
Изм.	Кол.уч.	Лист	№ док.	Подпись	Дата	Тип 1 Многоквартирные жилые дома 15-1, 15-2	Стадия	Лист	Листов
Разработал	Панкова				02.23		100.3		
Разработал	Панкова				02.23				
					02.23				
					02.23				
						План 2 этажа на отм. +3,000 (вариант планировочного решения)	 РЕГИСТРИРОВАННАЯ ФИРМА www.hrustalnyi.ru	№ СРО-П-201-04062018 -3827046991-277	

План 3 этажа на отм. +6,000

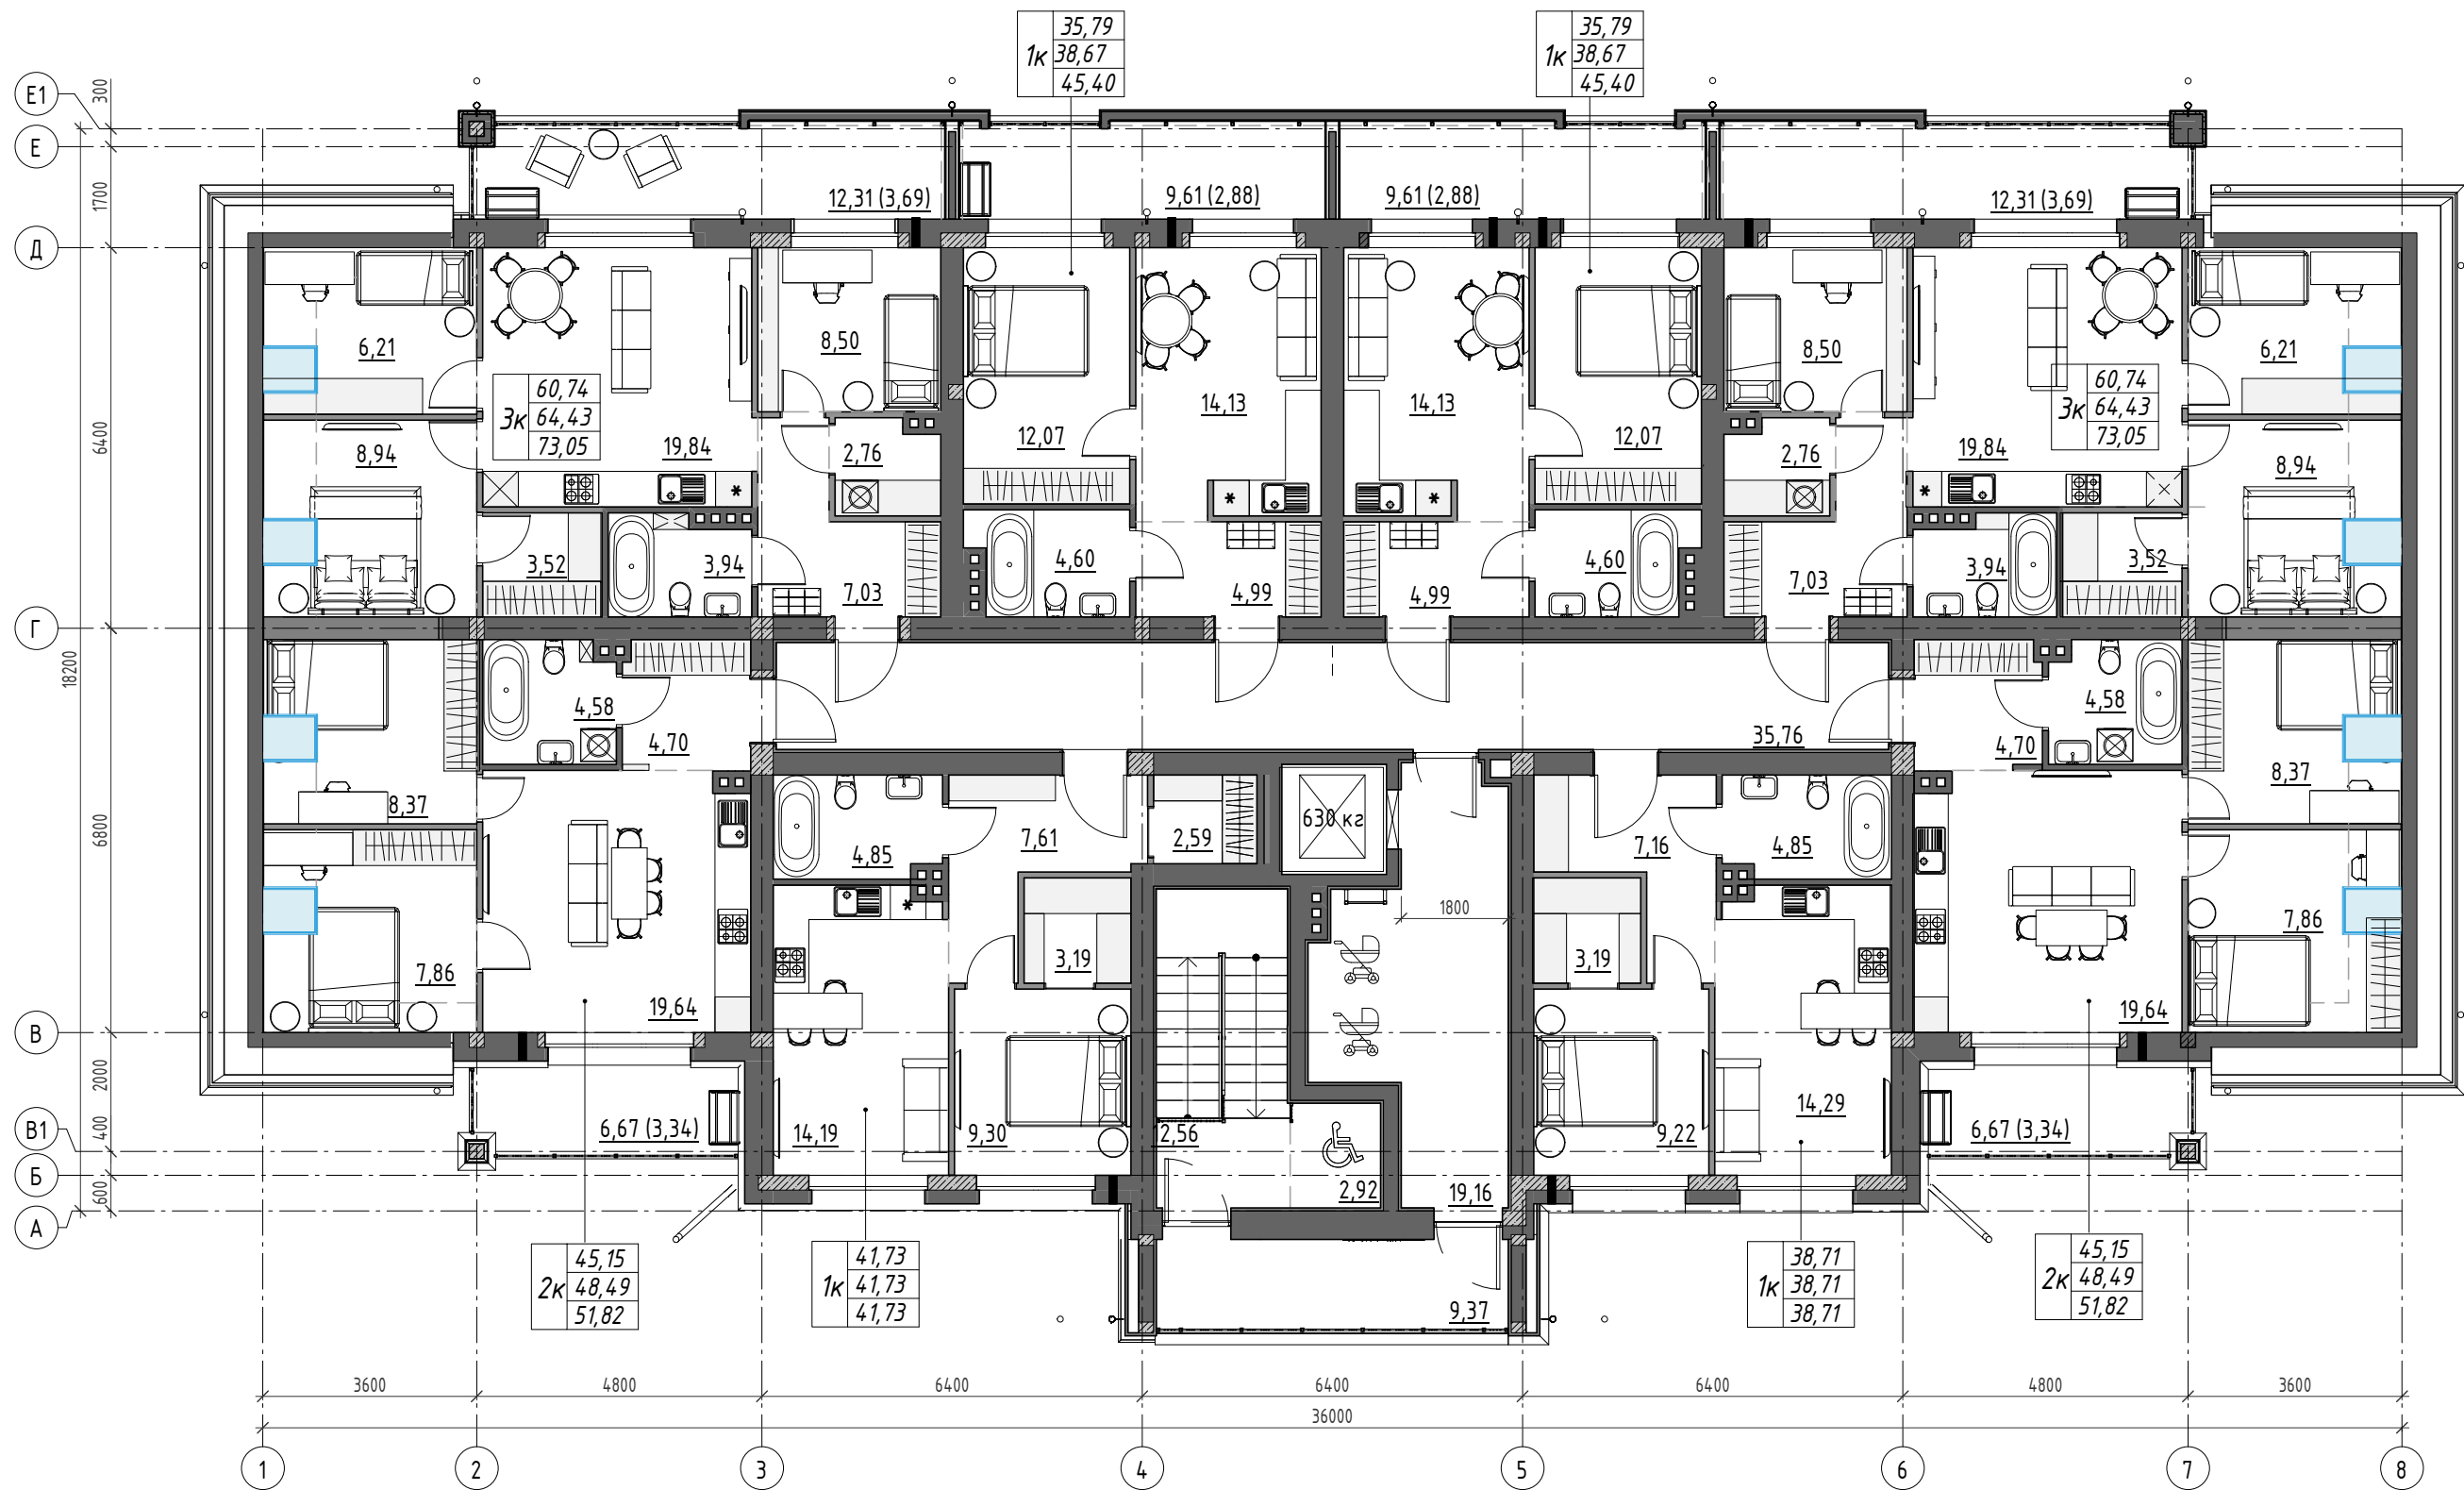

Взам. инв. №	
Подпись и дата	
Инв. № подл.	

						ХП.15-1 – АР			
						Микрорайон «Хрустальный Парк» и объекты инженерной инфраструктуры, расположенные на 11 км Байкальского тракта. 15-я очередь строительства (квартал “Датский”)			
Изм.	Кол.уч.	Лист	№ док.	Подпись	Дата	Тип 1 Множкквартирные жилые дома 15-1, 15-2	Стадия	Лист	Листов
Разработал	Панкова				02.23		100.4		
Разработал	Панкова				02.23				
					02.23				
					02.23				
						План 3 этажа на отм. +6,000 (вариант планировочного решения)		№СРО-П-201- 04062018 www.hrustalnyi.ru	-3827046991-277